

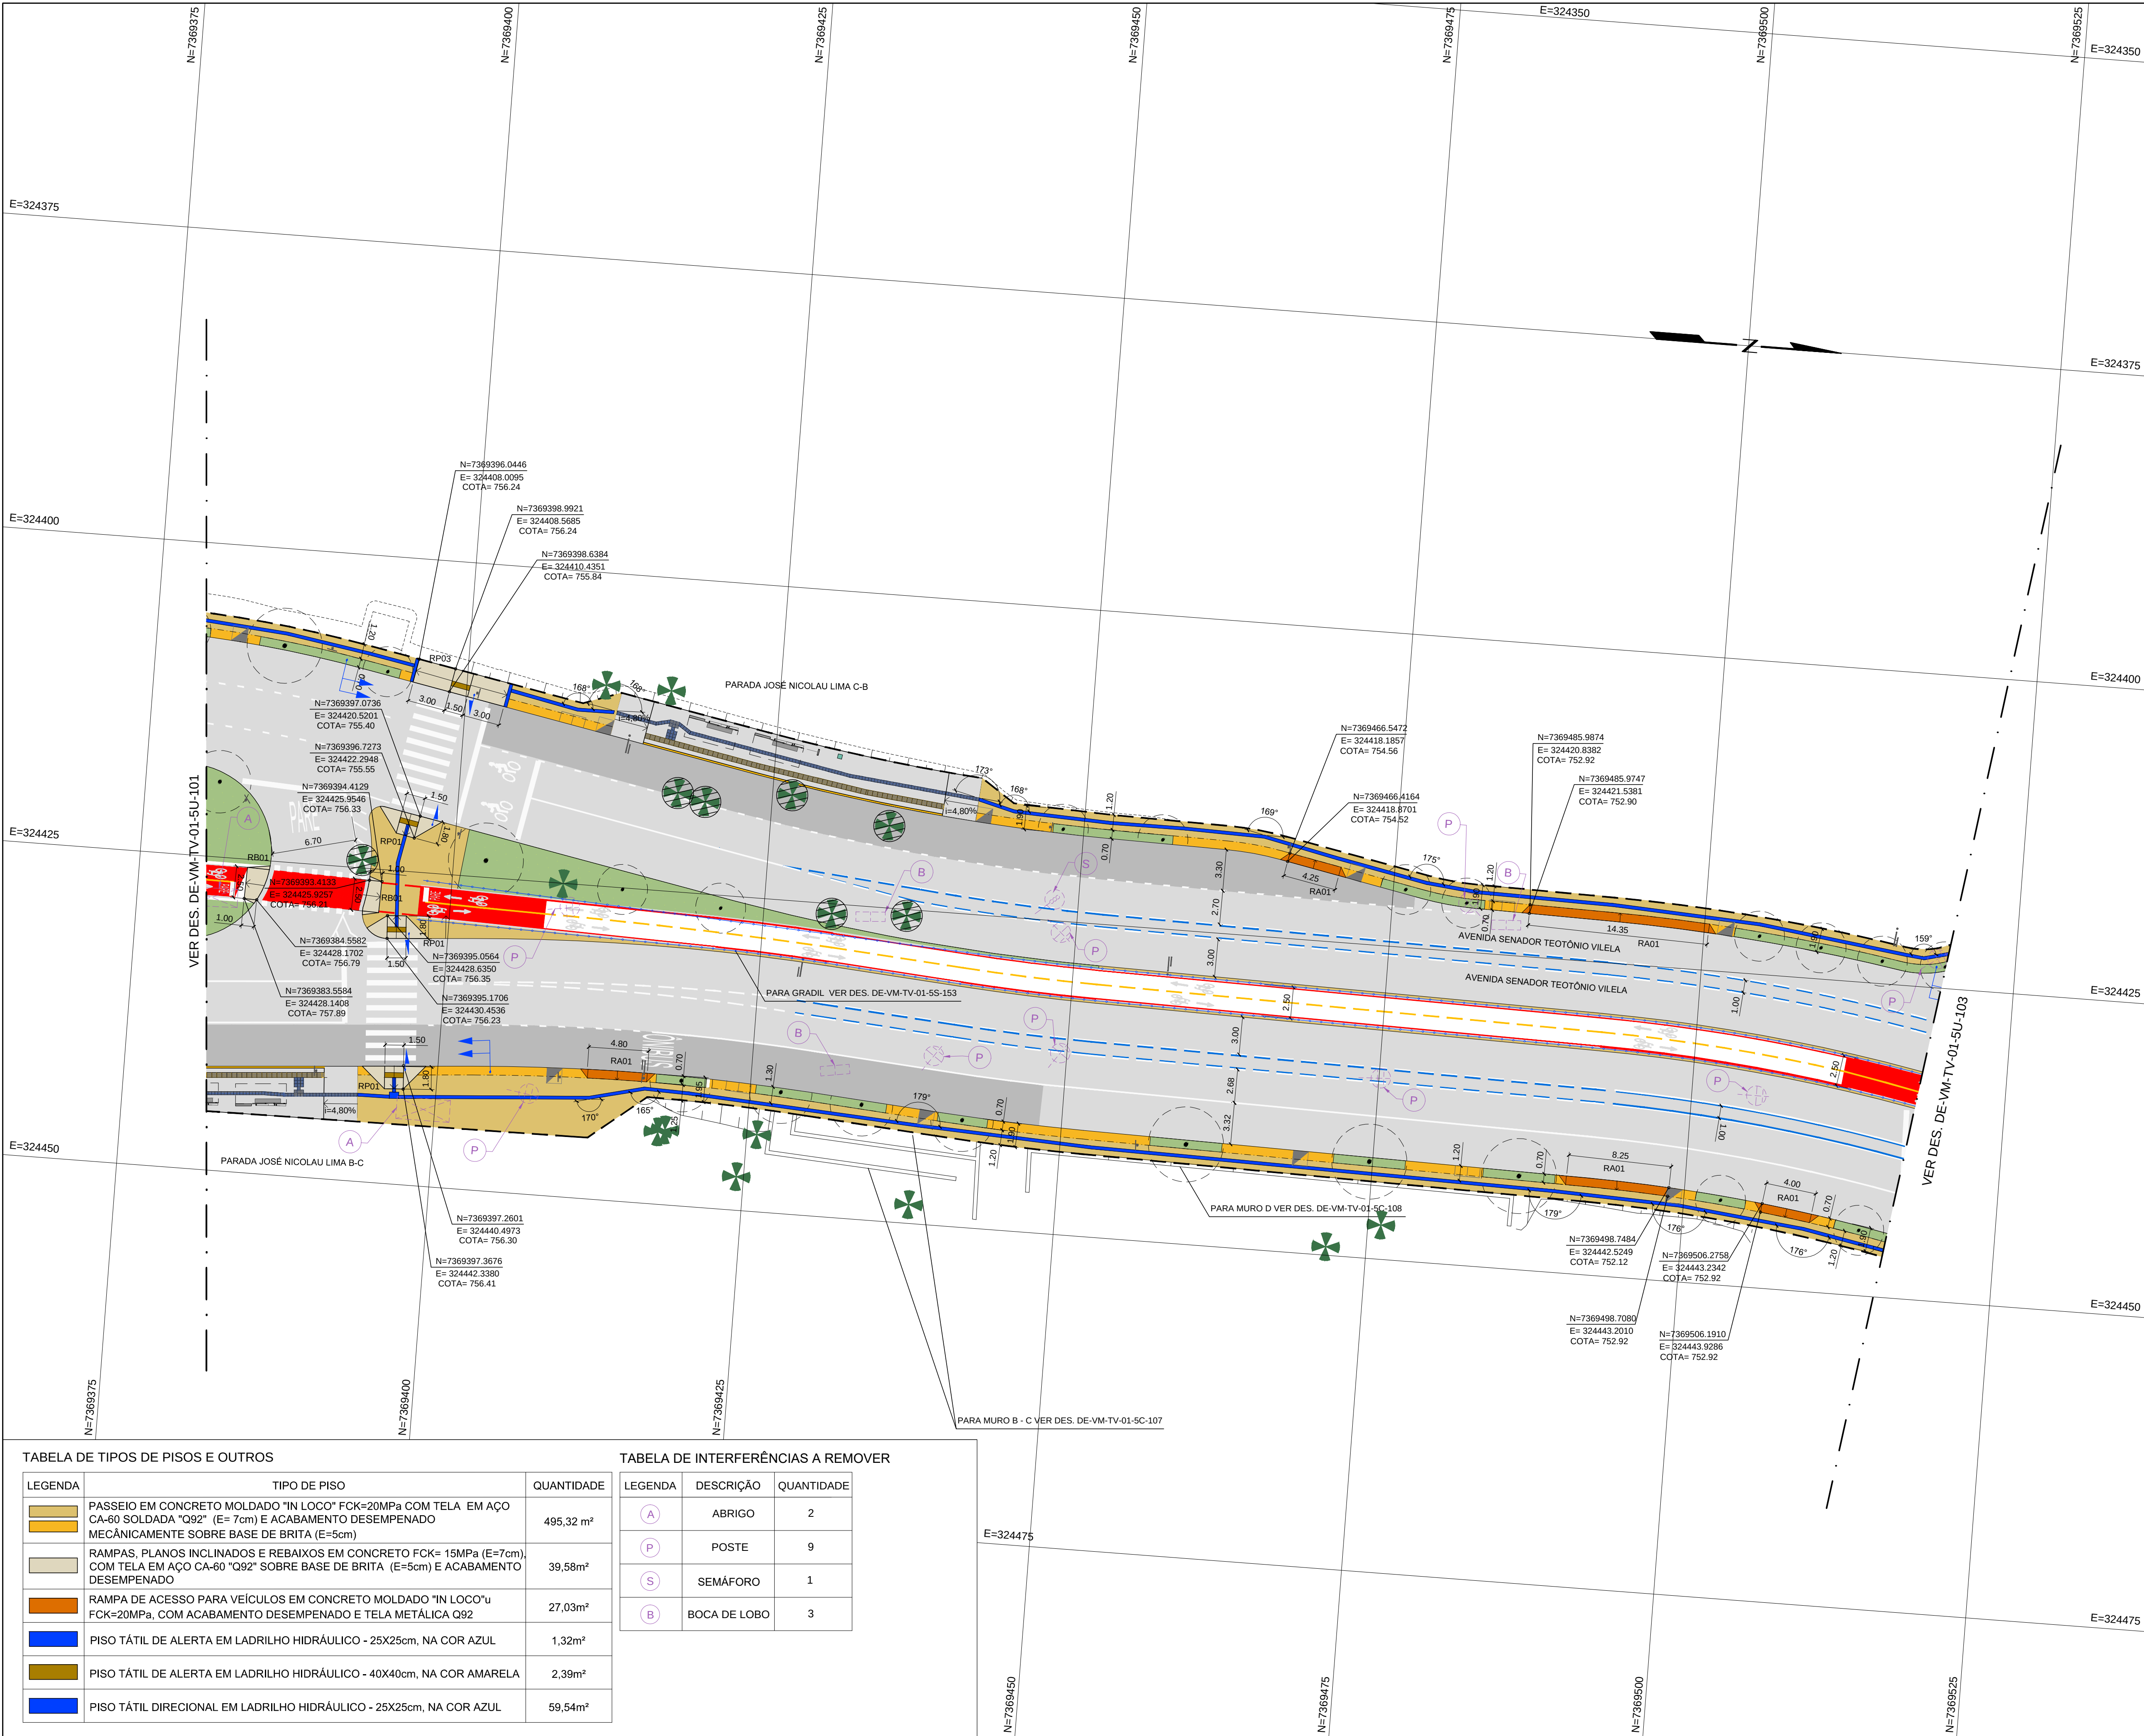


TABELA DE TIPOS DE PISOS E OUTROS

LEGENDA	TIPO DE PISO	QUANTIDADE
	PASSEIO EM CONCRETO MOLDADO "IN LOCO" FCK=20MPa COM TELA EM AÇO CA-60 SOLDADA "Q92" (E= 7cm) E ACABAMENTO DESEMPENADO MECÂNICAMENTE SOBRE BASE DE BRITA (E=5cm)	495,32 m²
	RAMPAS, PLANOS INCLINADOS E REBAIXOS EM CONCRETO FCK= 15MPa (E=7cm), COM TELA EM AÇO CA-60 "Q92" SOBRE BASE DE BRITA (E=5cm) E ACABAMENTO DESEMPENADO	39,58m²
	RAMPA DE ACESSO PARA VEÍCULOS EM CONCRETO MOLDADO "IN LOCO"u FCK=20MPa, COM ACABAMENTO DESEMPENADO E TELA METÁLICA Q92	27,03m²
	PISO TÁTIL DE ALERTA EM LADRILHO HIDRÁULICO - 25X25cm, NA COR AZUL	1,32m²
	PISO TÁTIL DE ALERTA EM LADRILHO HIDRÁULICO - 40X40cm, NA COR AMARELA	2,39m²
	PISO TÁTIL DIRECIONAL EM LADRILHO HIDRÁULICO - 25X25cm, NA COR AZUL	59,54m²

TABELA DE INTERFERÊNCIAS A REMOVER


LEGENDA	DESCRIÇÃO	QUANTIDADE
	ABRIGO	2
	POSTE	9
	SEMÁFORO	1
	BOCA DE LOBO	3

NOTAS:
1- MEDIDAS EM METRO, EXCETO ONDE INDICADO.
2- PARA AS ROTAS DE PISO PODOTÁTIL FORAM CONSIDERADAS AS
- NBR 16.537/2018 QUE DISPÕE SOBRE ACESSIBILIDADE - SINALIZAÇÃO TÁTIL DE PISO - DIRETRIZES PARA ELABORAÇÃO DE PROJETOS E INSTALAÇÃO.
- NBR 9050/2021 QUE DISPÕE SOBRE ACESSIBILIDADE A EDIFICAÇÕES, MOBILIÁRIO, ESPAÇOS E EQUIPAMENTOS URBANOS;
3- PARA DETALHES DE RAMPA VER FOLHAS DE-VM-TV-014U-007-008;

LEGENDA:

- PISTA
- CORREDOR DE ÔNIBUS
- CICLOVIA
- FAIXA LIVRE
- FAIXA DE ACESSO
- ALINHAMENTO DOS LOTES
- FAIXA AZUL SINALIZAÇÃO
- SEMÁFORO
- PLACAS
- ILUMINAÇÃO
- ÁRVORE PROPOSTA
- CANTEIRO PROPOSTO
- ÁRVORE EXISTENTE A MANTER
- ÁRVORE EXISTENTE A REMOVER
- GRADIL PROPOSTO

ARTICULAÇÃO:

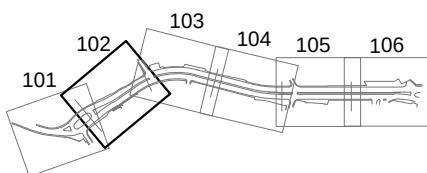

REVISÃO	VISTO PROJETISTA	DATA	VISTO SP OBRAS	DATA
H	FABIOLA	23/06/2026		
G	FABIOLA	18/12/2025		
F	FABIOLA	13/06/2025		
E	FABIOLA	20/09/2024		
D	FABIOLA	16/07/2024		
C	FABIOLA	20/06/2024		
B	FABIOLA	03/04/2024		
A	FABIOLA	04/03/2024		

DESENHOS DE REFERÊNCIA

DE-VM-TV-4F-101 A 103

DE-VM-TV-4F-151 A 153

DOCUMENTOS EXTERNOS DE REFERÊNCIA

DESENHO Nº

V M T V 0 1 5 U 1 0 2 H

SUBSTITUÍDO POR Nº

SUBSTITUÍ Nº

OBRA
DUPLICAÇÃO VIÁRIA DA AV. SEN. TEOTONIO VILELA.

TÍTULO

PROJETO EXECUTIVO DE URBANISMO - PLANTA

ESCALA



1000-SI060-015-UB3-102_G

RESPONSÁVEL TÉCNICO
LEONARDO P. LORENZO

CREA
0601838572

VISTO		DATA
PROJETO	FABIOLA AVAMILENO	MAR/2024
DESENHO	FABIOLA AVAMILENO	MAR/2024
VERIFICAÇÃO	ENNIO PASSAFINI	MAR/2024
APROVAÇÃO	JULIANA GODOI	MAR/2024
LIBERAÇÃO	LEONARDO P. LORENZO	MAR/2024

SP Obras
CONSTRUINDO A SÃO PAULO DO FUTURO

ESTE DESENHO É PROPRIEDADE DA SP OBRAS. NÃO PODENDO SER REPRODUZIDO E/OU REVELADO NO TODO OU EM PARTE SEM SUA AUTORIZAÇÃO.

APROVAÇÃO FINAL	DATA
VERIFICAÇÃO	
APROVAÇÃO	
LIBERAÇÃO	