


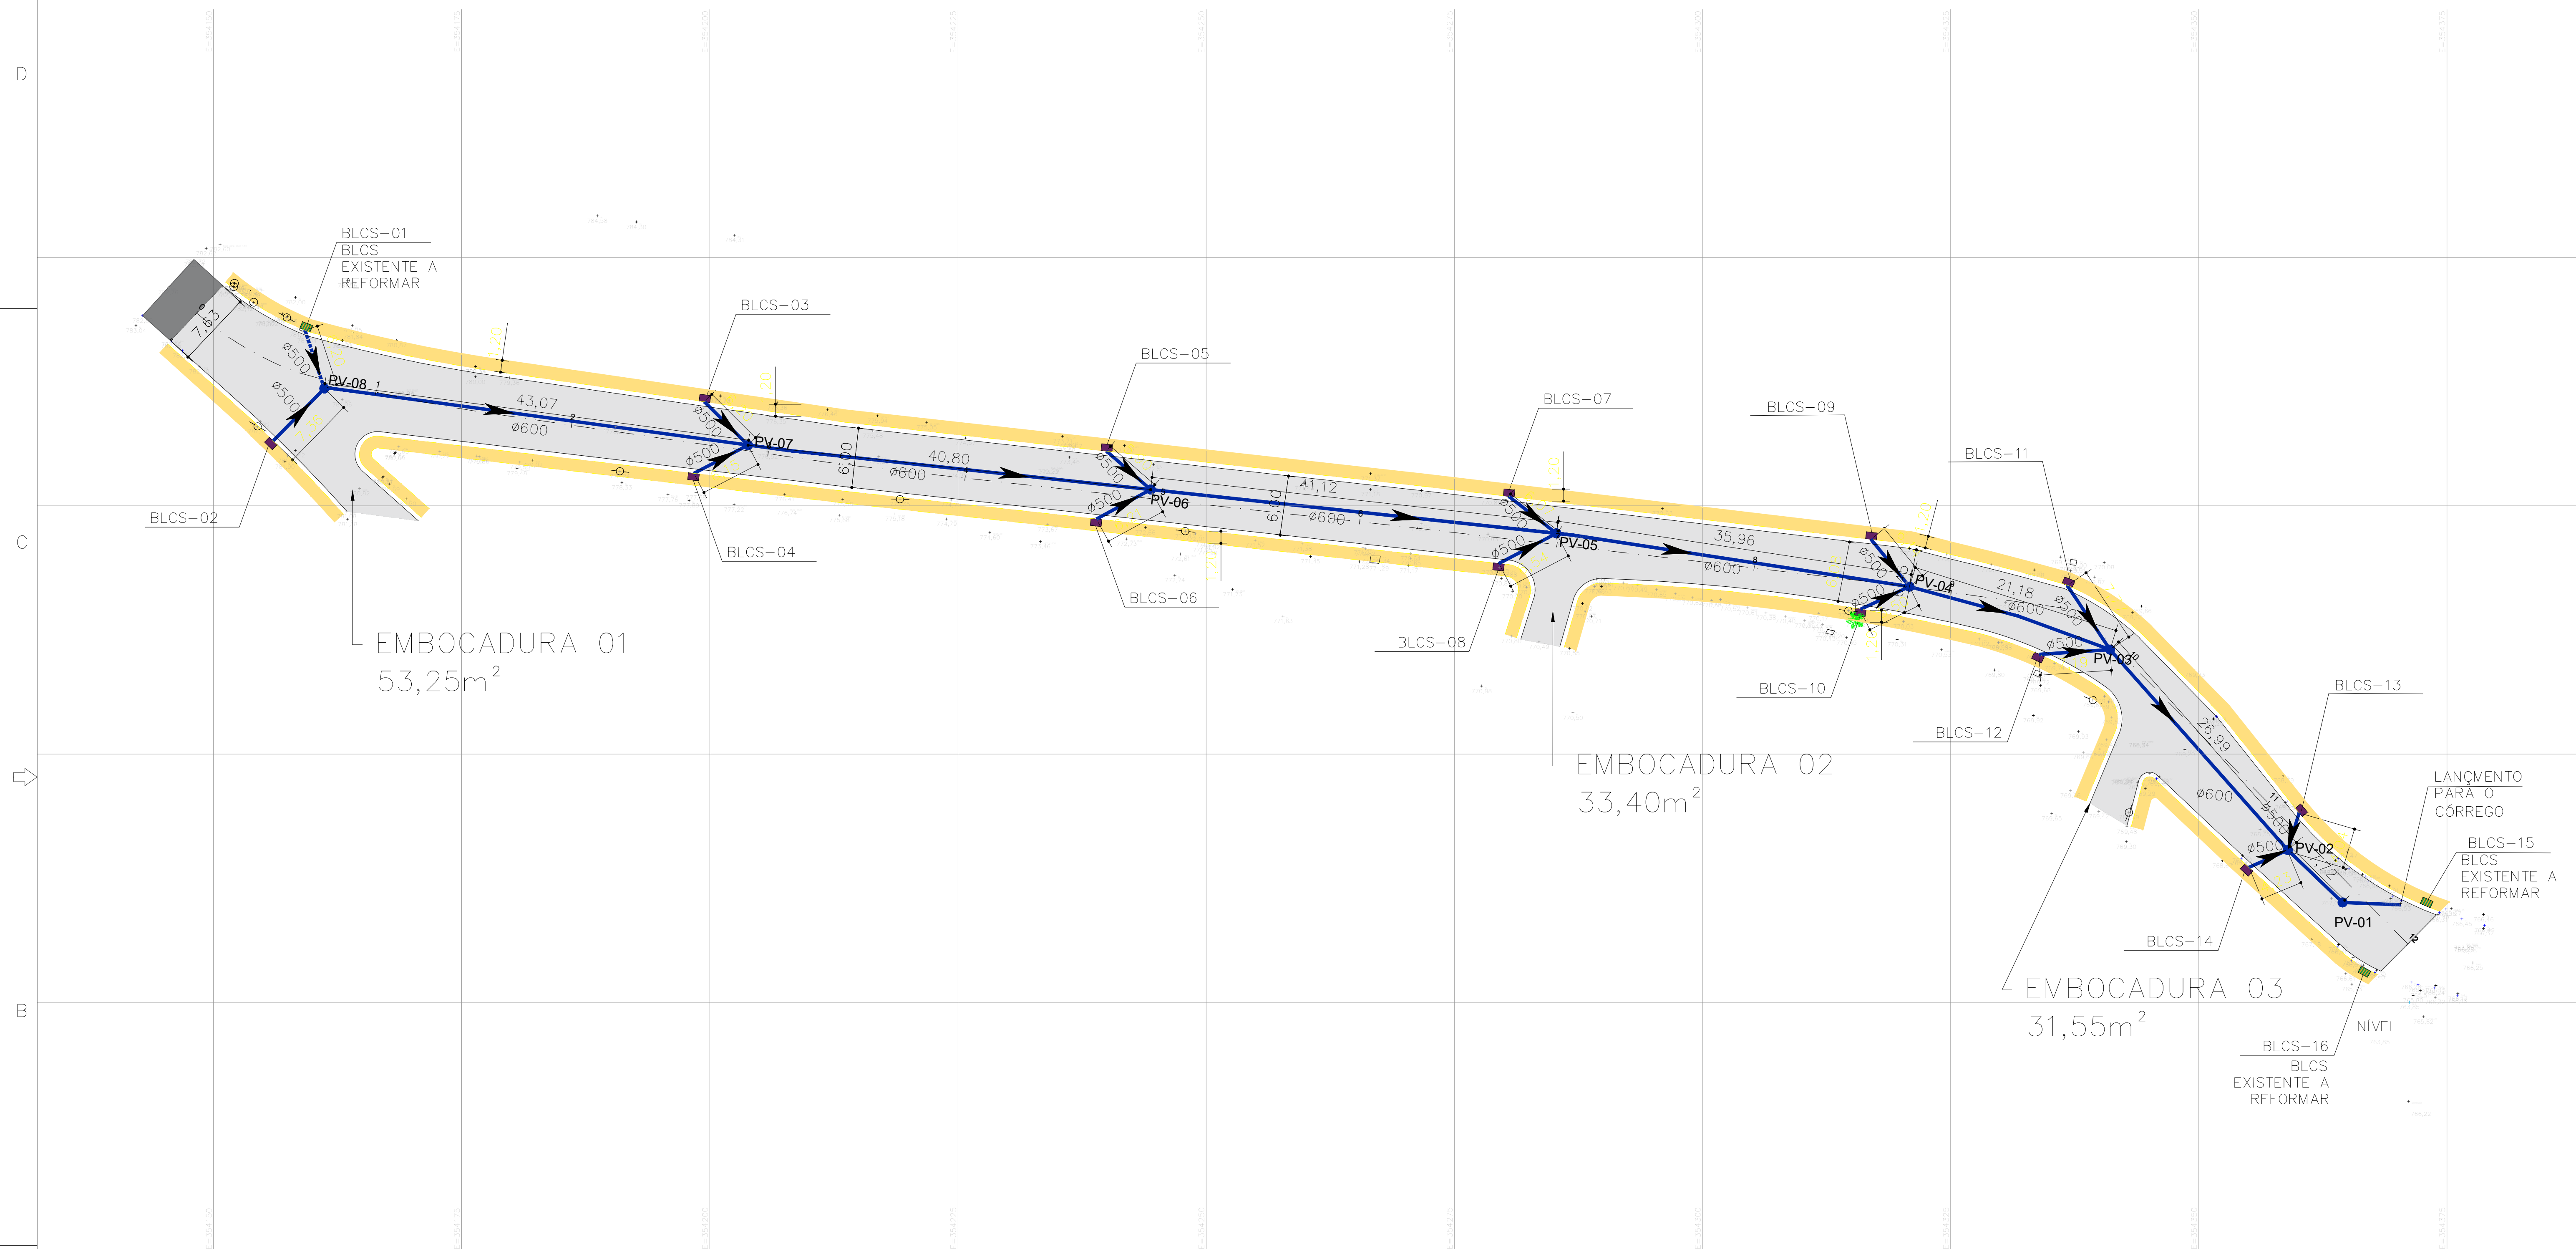


QUADRO DE QUANTIDADES					
DESCRIÇÃO/ITEM				QTD	UNID
FORNECIMENTO E ASSENTAMENTO DE TUBOS DE CONCRETO					
1	BSTC-CONCRETO SIMPLES (D=0,50 m)			85,00	m
2	BSTC-CONCRETO ARMADO – TIPO PA2 (D=0,60 m)			222,00	m
3	BSTC- CONCRETO ARMADO (D=0,80 m)			0,00	m
4	PV-TIPO 1 (1,40X1,40X1,40)			8,00	un
5	PV-ESPECIAL			0,00	un
6	BLCS-BOCA DE LOBO SIMPLES			16,00	un
7	CONSTRUÇÃO DE SARIJÊÃO			0,00	m³

REVISÃO N°	DATA	NATUREZA DA REVISÃO	EXECUÇÃO	VERIFICAÇÃO	APROVAÇÃO	DOCUMENTO DE REFERÊNCIA	DATA	FIRMA	N° DESENHO

LEGENDA:

- SARJETAS
- - - GUIAS
- XX ESTAQUEAMENTO
- POÇOS DE VISITA
- TUBULAÇÃO
- SENTIDO DO ESCOAMENTO DA ÁGUA

 BLCS – BOCA DE LOBO SIMPLES A SER CONSTRUÍDA
 BLCS – BOCA DE LOBO SIMPLES A SEREM REFORMADAS
 TUBULAÇÃO EXISTENTE

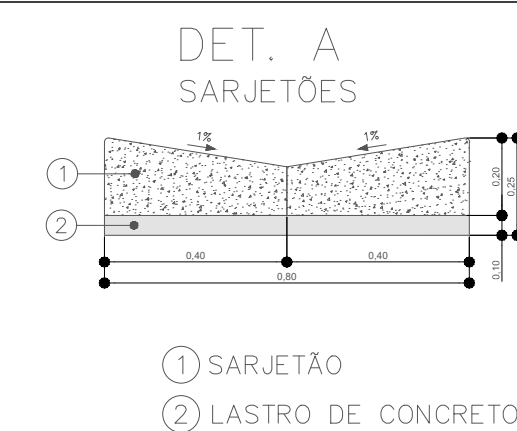

DESENHO* N- CT-AS-102-1001-0F-DE	ESCALA 1:500
PROJETO	
DESENHO	
VERIFICAÇÃO	
APROVAÇÃO	
AUTORIZAÇÃO	

SUBPREFEITURA DE ITAQUERA

OBJETO	OPERAÇÃO	
	TRABALHO	
	DES. N°	01
	DATA	REV.
IMPLANTAÇÃO DE MELHORIAS NO SISTEMA VIÁRIO DA R. AGRIMENSOR SUGAYA SUB-TRECHO: AV. JACU-PESSEGO E A EST. CAMPOS DOS GOITACAZES	01/07/2026	OF
PROJETO DE DRENAGEM		