

D

C

B



A

E=348050

E=348100

E=348150

E=348200

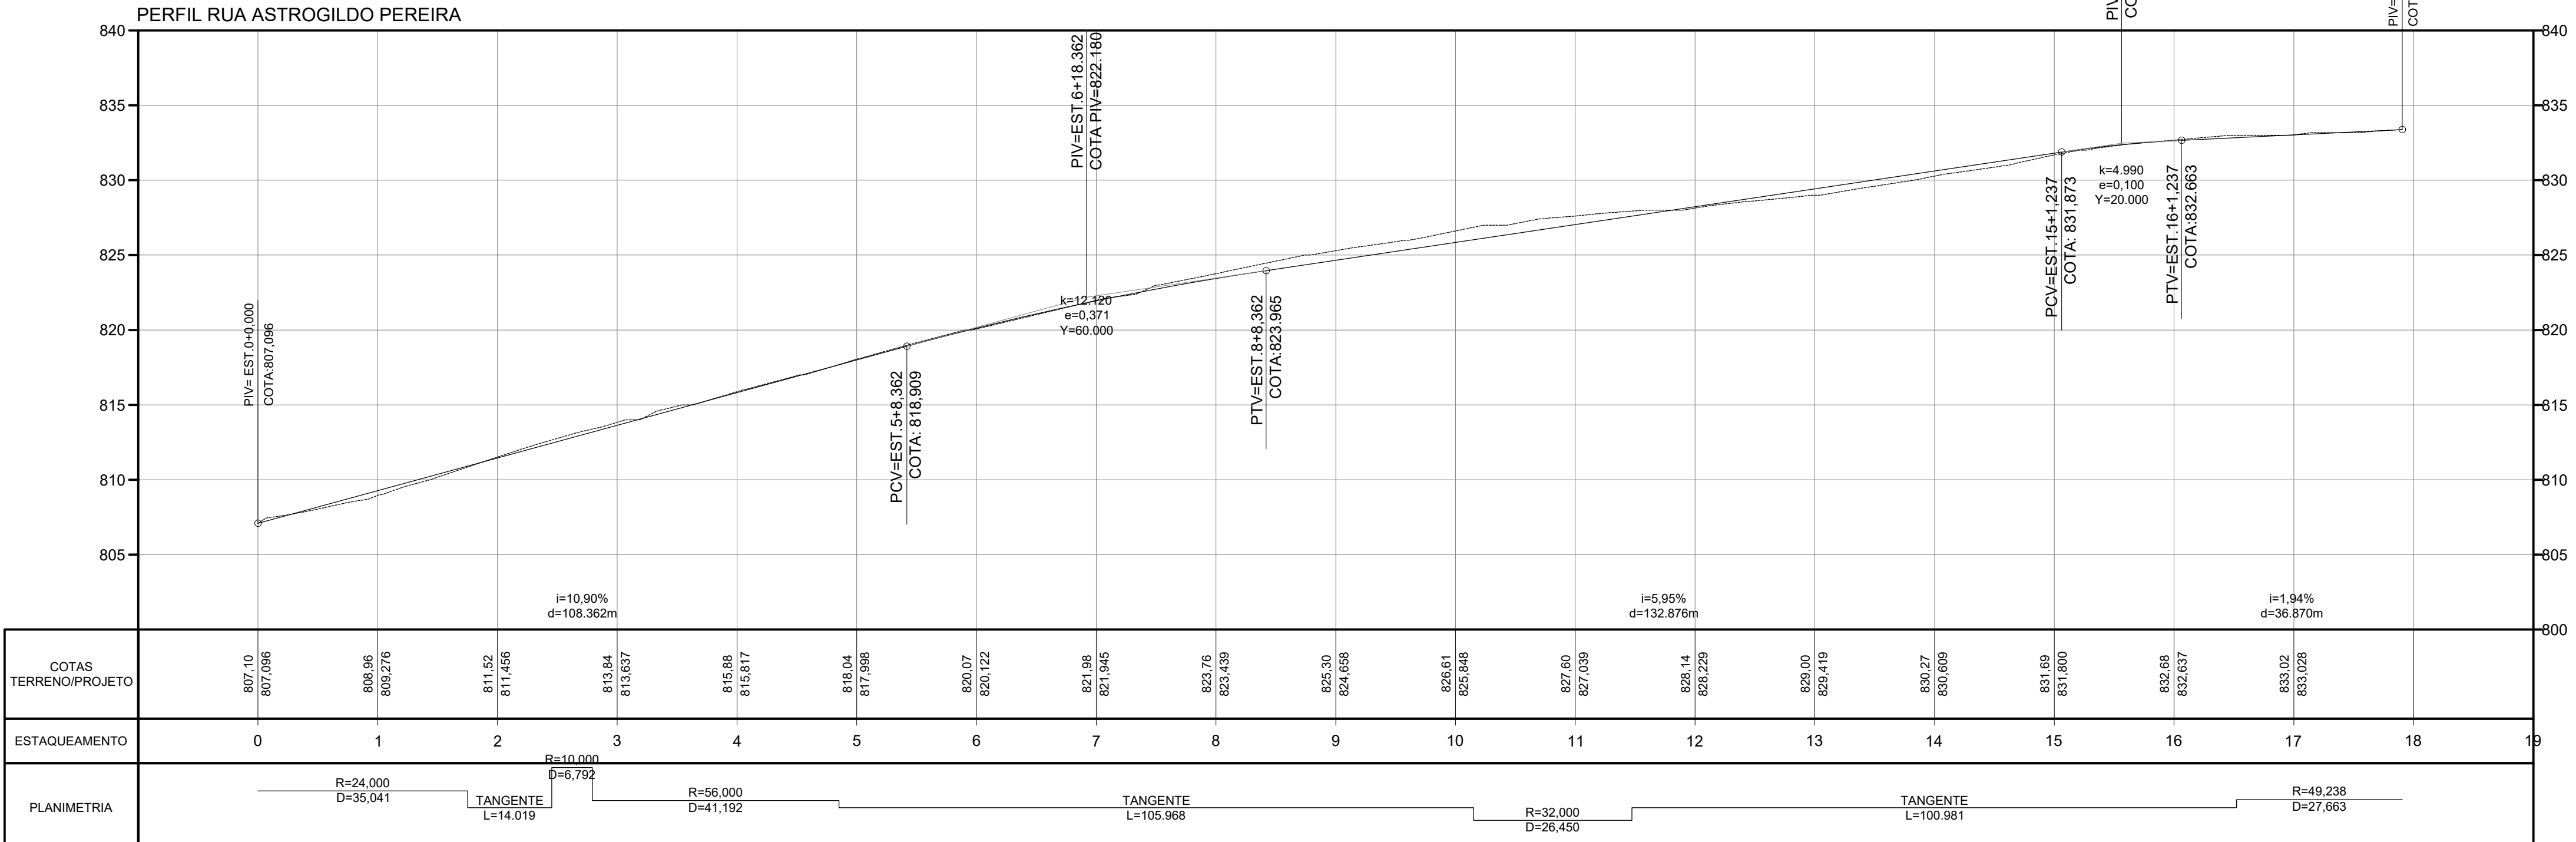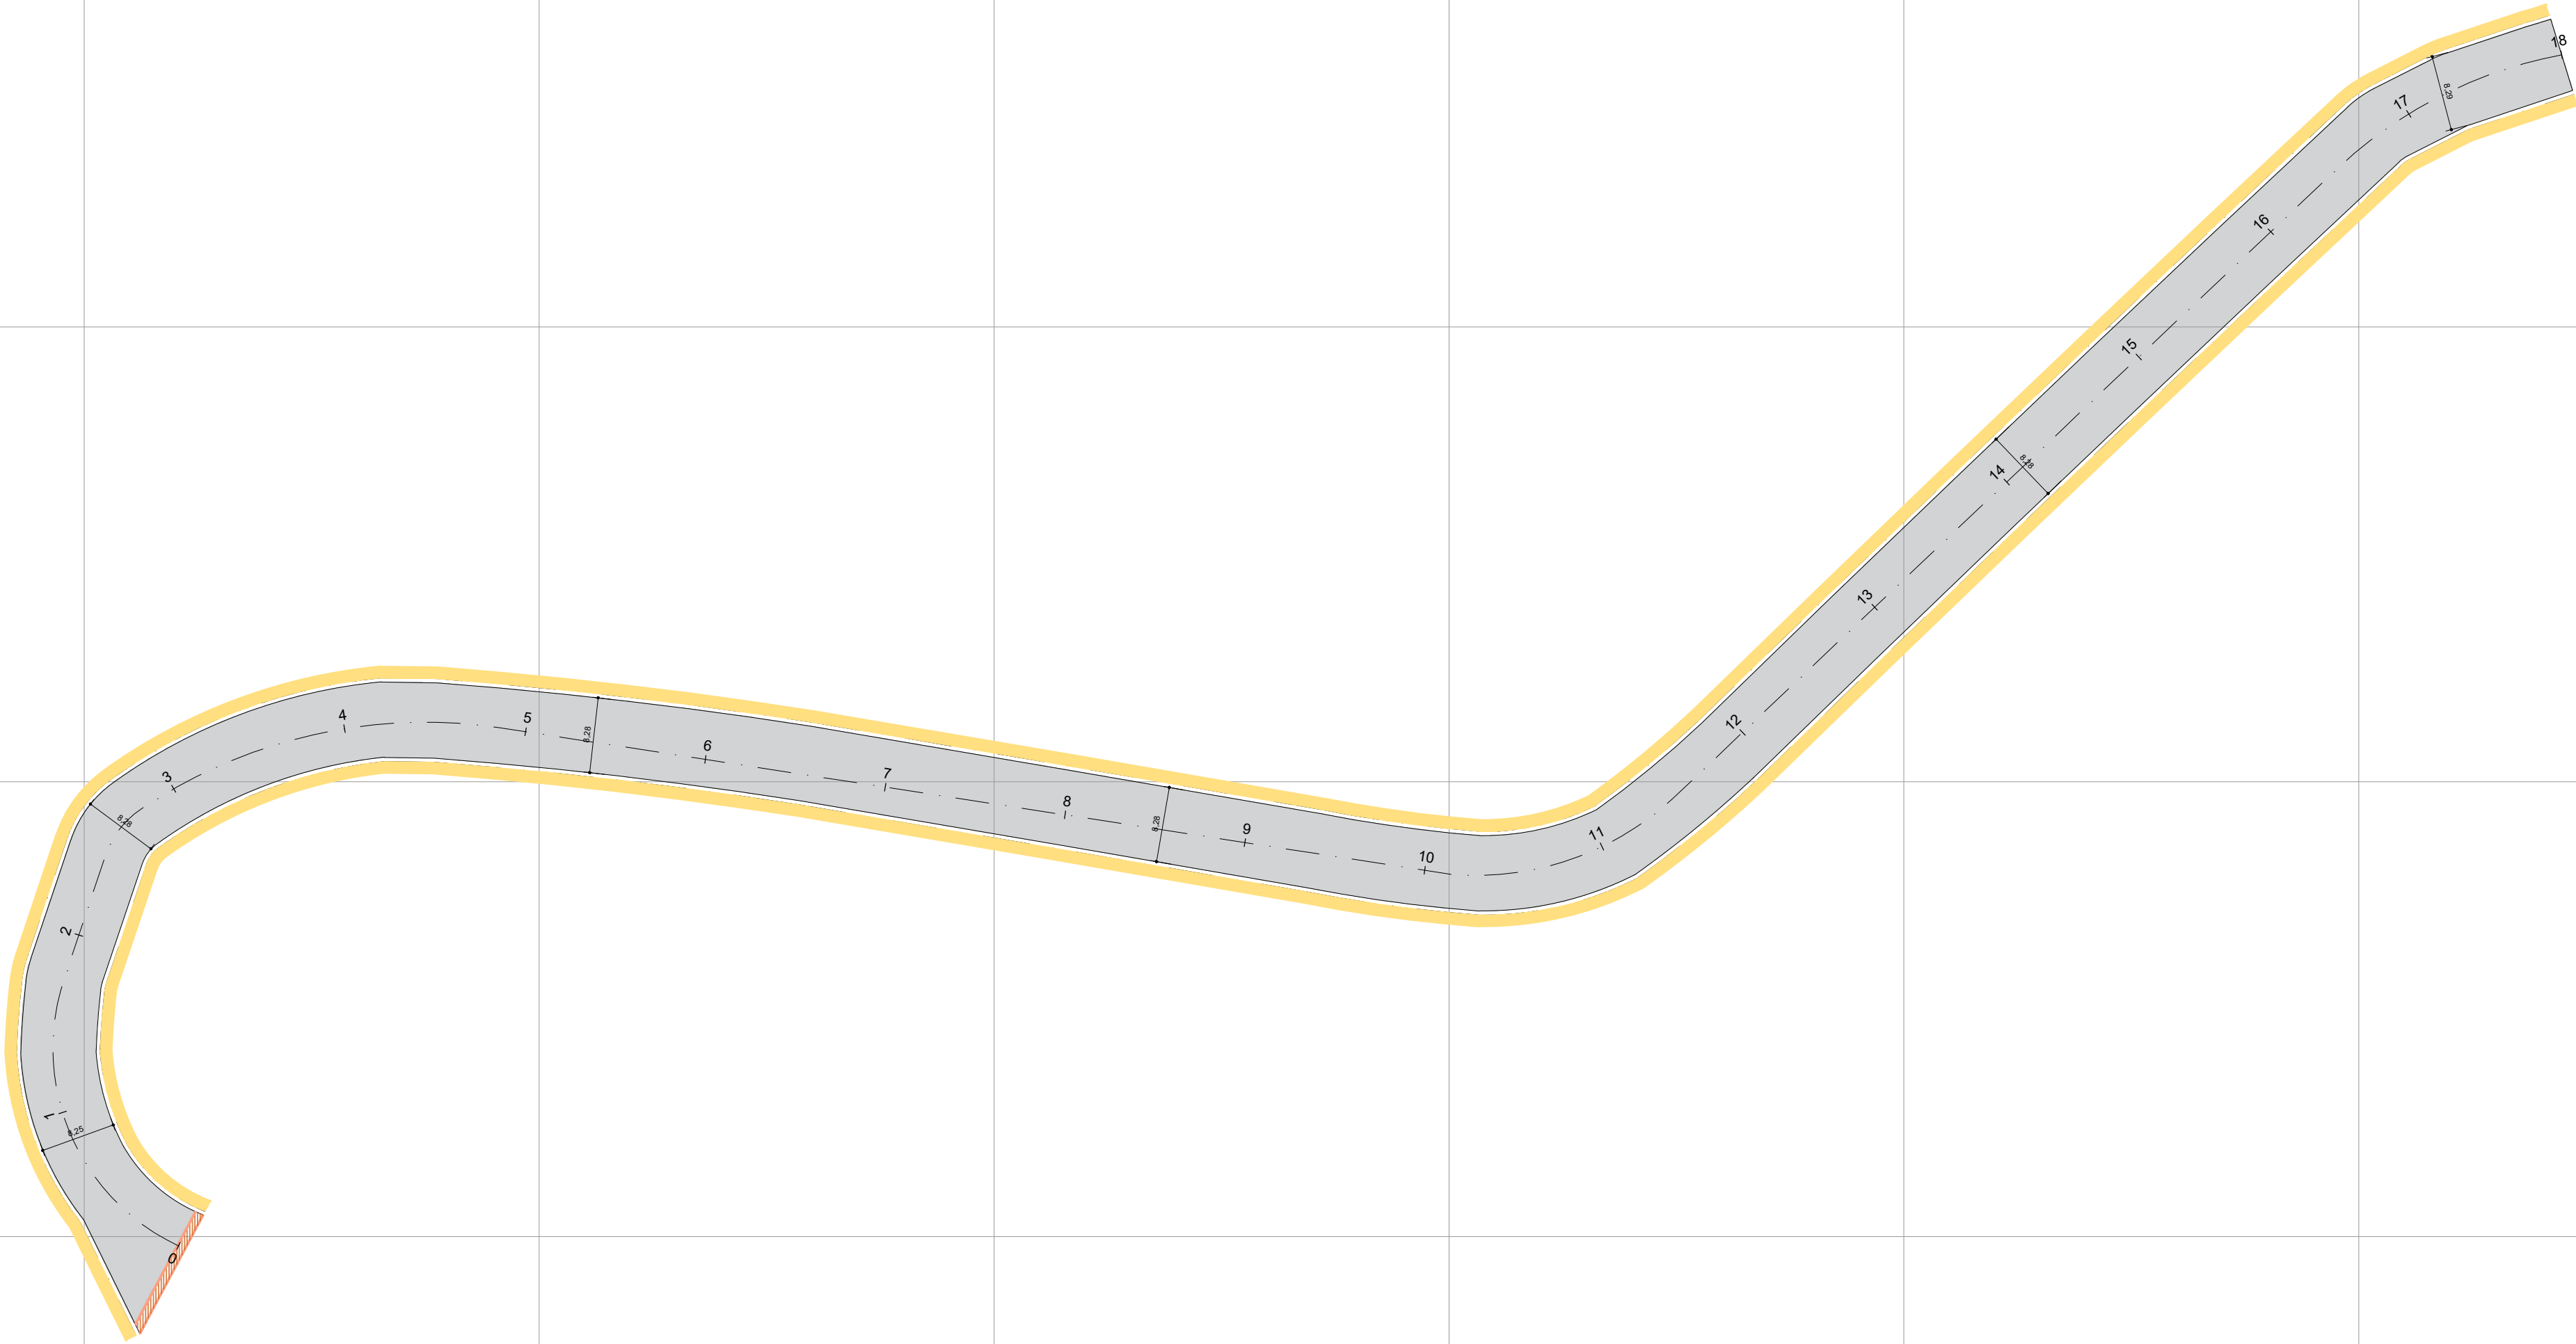

LEGENDA:
— SARJETAS
- - - GUIAS
XX ESTAQUEAMENTO

DESENHO* N—
CT—AP—103—1001—OG—DE
PROJETO
DESENHO
VERIFICAÇÃO
APROVAÇÃO
AUTORIZAÇÃO

ESCALA
1:500

SUBPREFEITURA DE ITAQUERA

OBJETO
IMPLANTAÇÃO DE MELHORIAS NO SISTEMA VIÁRIO DA R. ASTROGILDO PEREIRA
SUB—TRECHO: AV. ALZIRO ZARUR E A R. ASTROGILDO PEREIRA
PROJETO DE TERRAPLENAGEM

OPERAÇÃO	TRABALHO
DES. N°	01
DATA	30/06/2026
REV.	0F

REVISÃO N°	DATA	NATUREZA DA REVISÃO	EXECUÇÃO	VERIFICAÇÃO	APROVAÇÃO	DOCUMENTO DE REFERÊNCIA	DATA	FIRMA	N° DESENHO
------------	------	---------------------	----------	-------------	-----------	-------------------------	------	-------	------------