
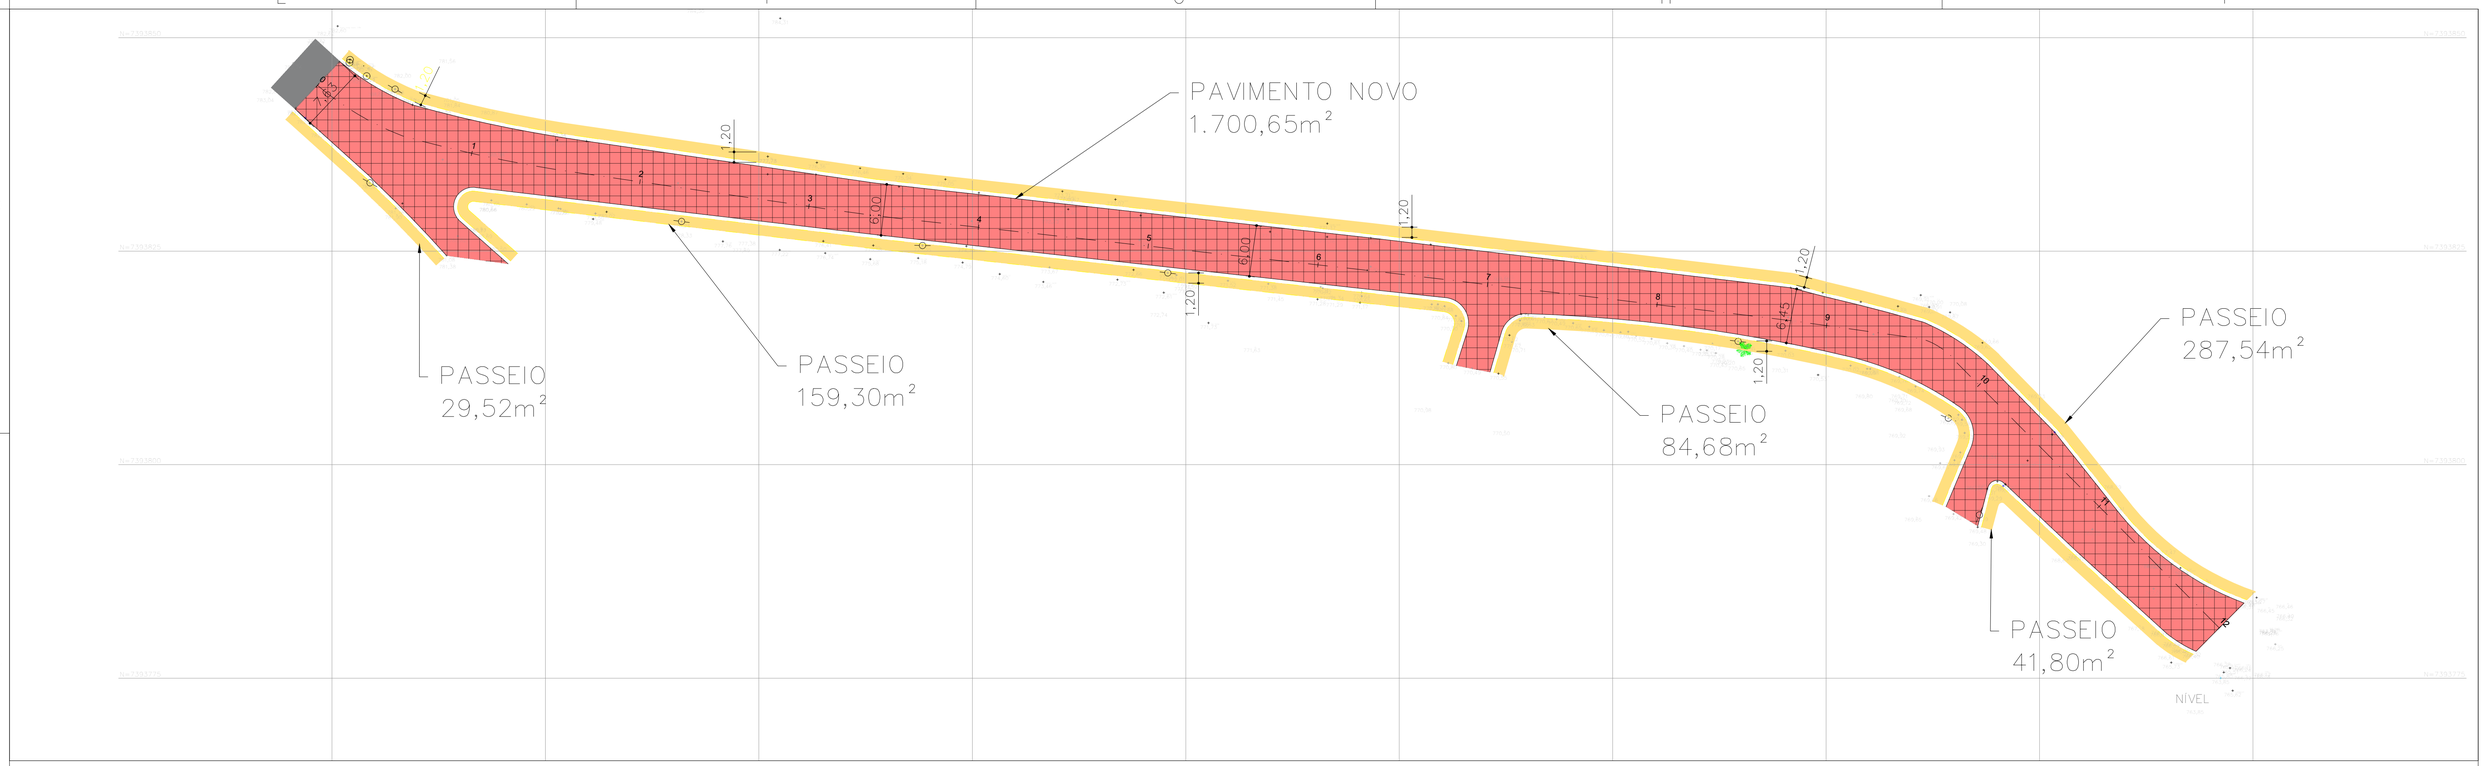


HSL p/ CBR=		
MATERIAL	Esp. (cm)	Representação Gráfica
PRE-MISTURADO À QUENTE	5,0	
IMPRIMAÇÃO LIGANTE	–	
PRÉ-MISTURADO À QUENTE	5,0	
IMPRIMAÇÃO LIGANTE	–	
MACADAME BETUMINOSO	15,0	
IMPRIMAÇÃO IMPERMEABILIZANTE	–	
MACADAME HIDRÁULICO	15,0	
SOLO MELHORADO COM AGREGADO 10% EM VOLUME	20,0	
SUBLEITO[1]	–	
TOTAL	–	

[1]COMPACTADO A 100% PN – CBR >4% – EXP <2%


QUADRO DE QUANTIDADES			
DADOS DAS VIA			
	DESCRIÇÃO	UNIDADE	UN
1.1	ÁREA TOTAL	1.700,65	m²
1.2	COMPRIMENTO DA VIA (ESTAQUEADA)	240,00	m
INFRAESTRUTURA			
2.1	ÁREA DE PASSEIO	602,86	m²
2.2	FORNECIMENTO E ASSENTAMENTO DE GUIA	512,00	m
PAVIMENTAÇÃO			
3.1	PAVIMENTAÇÃO – SEÇÃO B – PAVIMENTO NOVO	1.700,65	m²
3.2	DEMOLIÇÃO DE PAVIMENTO	1.700,65	m²

DET. A
SARJETAS

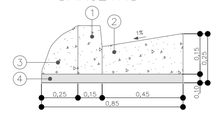

1. GUIA
2. SARJETA
3. BOLA DE CONCRETO
4. LASTRO DE CONCRETO

DET. B
PASSEIOS

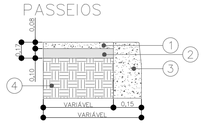

1. PASSEIOS
2. LASTRO DE CONCRETO
3. GUIAS
4. CAMADA EXISTENTE

REVISÃO Nº	DATA	NATUREZA DA REVISÃO	EXECUÇÃO	VERIFICAÇÃO	APROVAÇÃO	DOCUMENTO DE REFERÊNCIA	DATA	FIRMA	Nº DESENHO

LEGENDA:
- PAVIMENTAÇÃO – SEÇÃO B – A: 1.700,65 m²
- CONSTRUÇÃO DE PASSEIO – A: 602,86 m²
- DEMOLIÇÃO DE PAVIMENTO – A: 1.700,65 m²
- SARJETAS
- GUIAS
- XX ESTAQUEAMENTO
- POSTE

SUBPREFEITURA DE ITAQUERA

DESENHO Nº N– CT–AS–101–1001–0F–DE	ESCALA 1:500
PROJETO	
DESENHO	
VERIFICAÇÃO	
APROVAÇÃO	
AUTORIZAÇÃO	

OBJETO

IMPLANTAÇÃO DE MELHORIAS NO SISTEMA VIÁRIO DA R. AGRIMENSOR SUGAYA
SUB–TRECHO: AV. JACU–PÊSSEGO E A EST. CAMPOS DOS GOITACAZES

PROJETO DE PAVIMENTAÇÃO

OPERAÇÃO	
TRABALHO	
DES. Nº	01
DATA	01/07/2026
REV.	0F

A CÓPIA, TOTAL OU PARCIAL, DESTE DOCUMENTO É EXPRESSAMENTE PROIBIDA, CONFORME LEI Nº 9.610, DE FEVEREIRO DE 1998 – ART. 7º – LEI DE DIREITOS AUTORAIS.

CT–AS–101–1001–0F–DE.dwg