
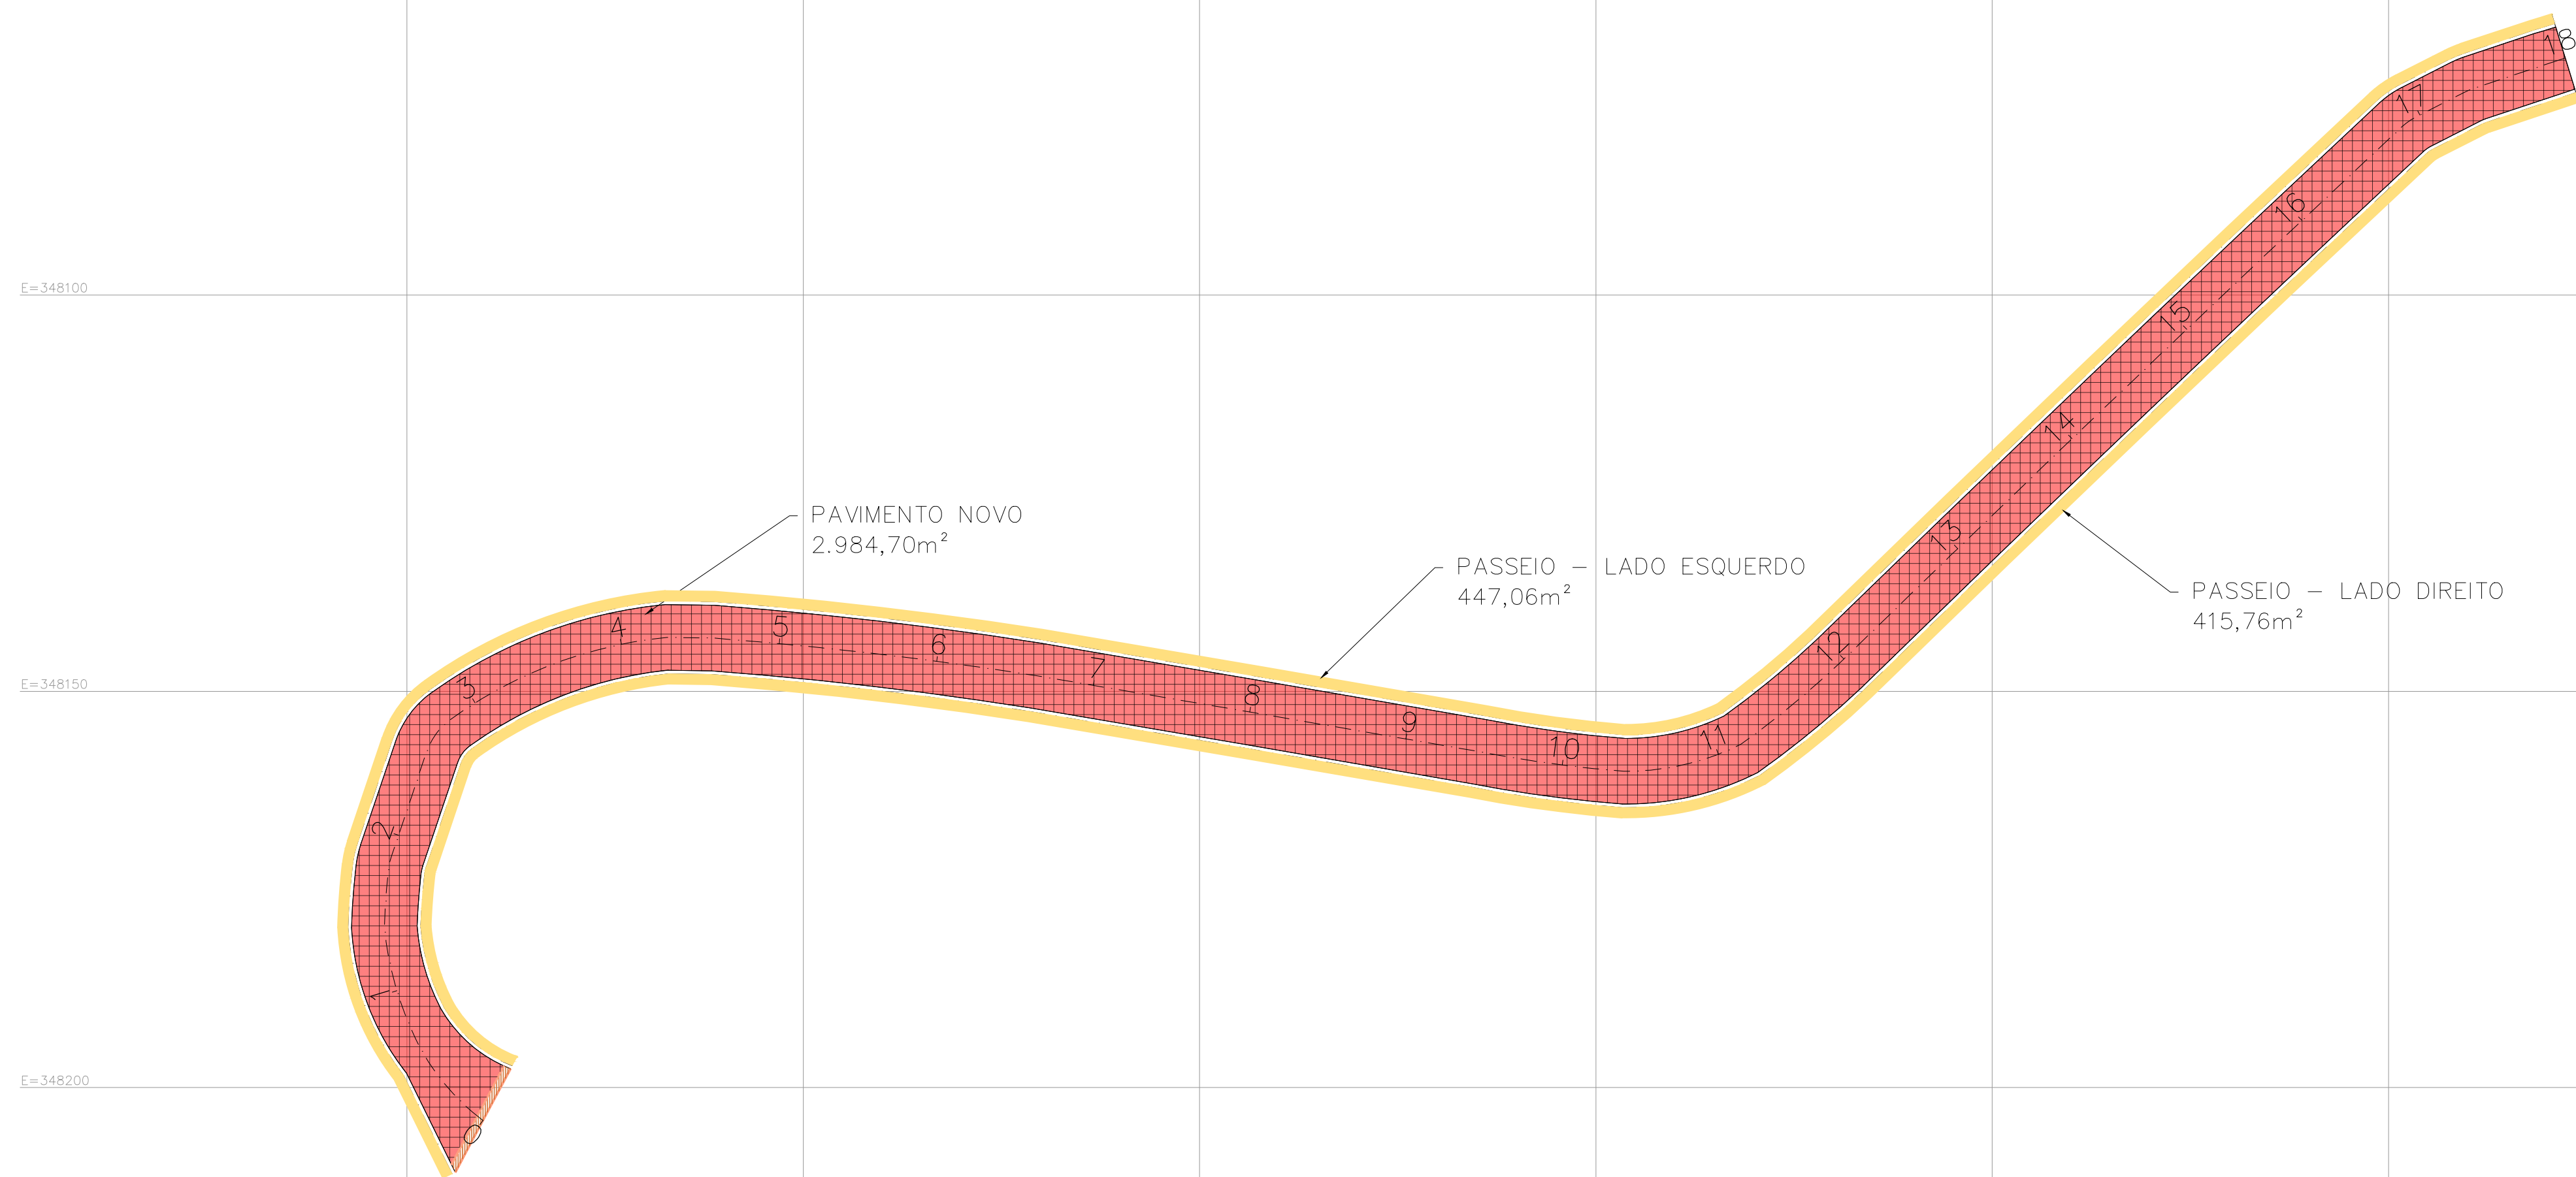
 
 
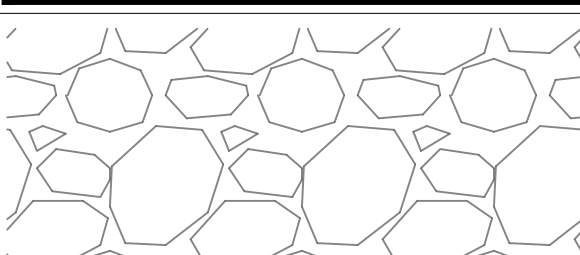
 
 
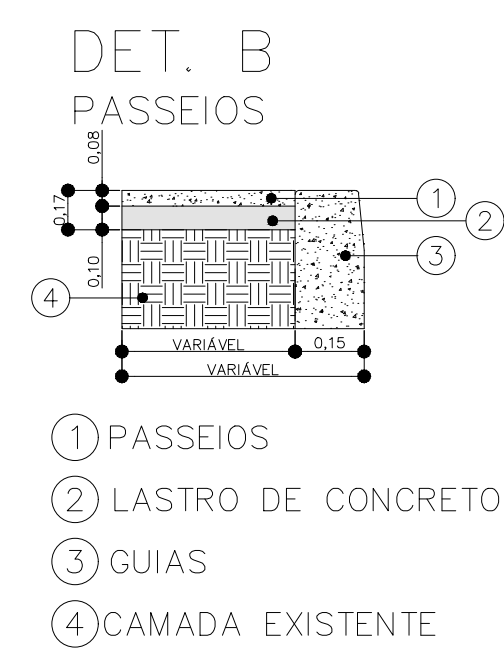


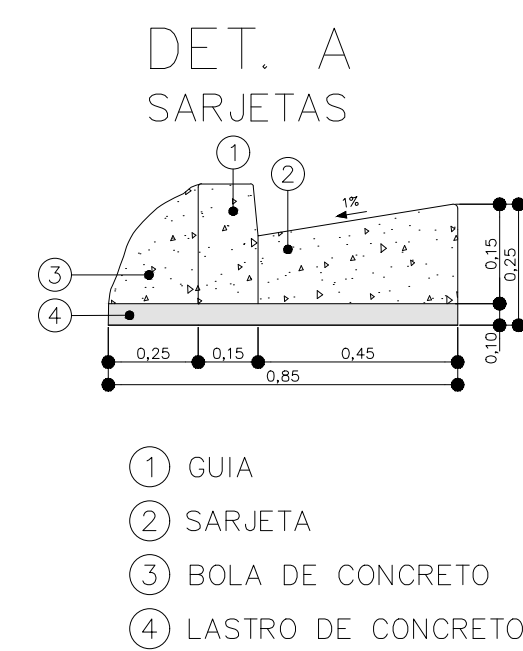

HSL p/ CBR=		
MATERIAL	Esp. (cm)	Representação Gráfica
PRE-MISTURADO À QUENTE	5,0	
IMPRIMAÇÃO LIGANTE	—	
PRÉ-MISTURADO À QUENTE	5,0	
IMPRIMAÇÃO LIGANTE	—	
MACADAME BETUMINOSO	15,0	
IMPRIMAÇÃO IMPERMEABILIZANTE	—	
MACADAME HIDRÁULICO	15,0	
SOLO MELHORADO COM AGREGADO 10% EM VOLUME	20,0	
SUBLEITO ¹	—	
TOTAL	—	

¹COMPACTADO A 100% PN - CBR >4% - EXP <2%

QUADRO DE QUANTIDADES			
DADOS DAS VIA			
	DESCRIÇÃO	UNIDADE	UN
1.1	ÁREA TOTAL	2.984,70	m ²
1.2	COMPRIMENTO DA VIA (ESTAQUEADA)	360,00	m
INFRAESTRUTURA			
2.1	ÁREA DE PASSEIO	862,83	m ²
2.2	FORNECIMENTO E ASSENTAMENTO DE GUIA	720,00	m
PAVIMENTAÇÃO			
3.1	PAVIMENTAÇÃO – SEÇÃO B – PAVIMENTO NOVO	2.984,70	m ²
3.2	DEMOLIÇÃO DE PAVIMENTO	2.984,70	m ²

[illegible]

LEGENDA:

 PAVIMENTAÇÃO - SEÇÃO B - A: 2.984,70 m²
 CONSTRUÇÃO DE PASSEIO - A: 862,83 m²
 DEMOLIÇÃO DE PAVIMENTO - A: 2.984,70 m²
 SARJETAS
 GUIAS
 ESTAKEAMENTO
 POSTE

DESENHO* N- CT-AP-101-1001-0G-DE	ESCALA 1:500
PROJETO	
DESENHO	
VERIFICAÇÃO	
APROVAÇÃO	
AUTORIZAÇÃO	

OBJETO

IMPLANTAÇÃO DE MELHORIAS NO SISTEMA VIÁRIO DA R. ASTROGILDO PEREIRA

SUB-TRECHO: AV. ALZIRO ZARUR E A R. ASTROGILDO PEREIRA

PROJETO DE PAVIMENTAÇÃO

OPERAÇÃO

TRABALHO

DES. N°

DATA

30/06/20