

TABELA DE TIPOS DE PISOS E OUTROS





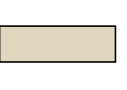
LEGENDA	TIPO DE PISO	QUANTIDADE
	PASSEIO EM CONCRETO MOLDADO "IN LOCO" FCK=20MPa COM TELA EM AÇO CA-60 SOLDADA "Q92" (E= 7cm) E ACABAMENTO DESEMPENADO MECÂNICAMENTE SOBRE BASE DE BRITA (E=5cm)	856,68m²
	RAMPAS, PLANOS INCLINADOS E REBAIXOS EM CONCRETO FCK= 15MPa (E=7cm), COM TELA EM AÇO CA-60 "Q92" SOBRE BASE DE BRITA (E=5cm) E ACABAMENTO DESEMPENADO	76,75m²
	RAMPA DE ACESSO PARA VEÍCULOS EM CONCRETO MOLDADO "IN LOCO" FCK=20MPa, COM ACABAMENTO DESEMPENADO E TELA METÁLICA Q92	54,00m²
	PISO TÁTIL DE ALERTA EM LADRILHO HIDRÁULICO - 25X25cm, NA COR AZUL	2,62m²
	PISO TÁTIL DE ALERTA EM LADRILHO HIDRÁULICO - 40X40cm, NA COR AMARELA	6,93m²
	PISO TÁTIL DIRECIONAL EM LADRILHO HIDRÁULICO - 25X25cm, NA COR AZUL	64,05m²

TABELA DE INTERFERÊNCIAS A REMOVER

LEGENDA	DESCRIÇÃO	QUANTIDADE
	ABRIGO	0
	POSTE	8
	SEMÁFORO	0
	BOCA DE LOBO	3

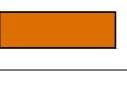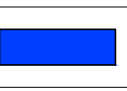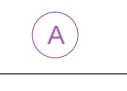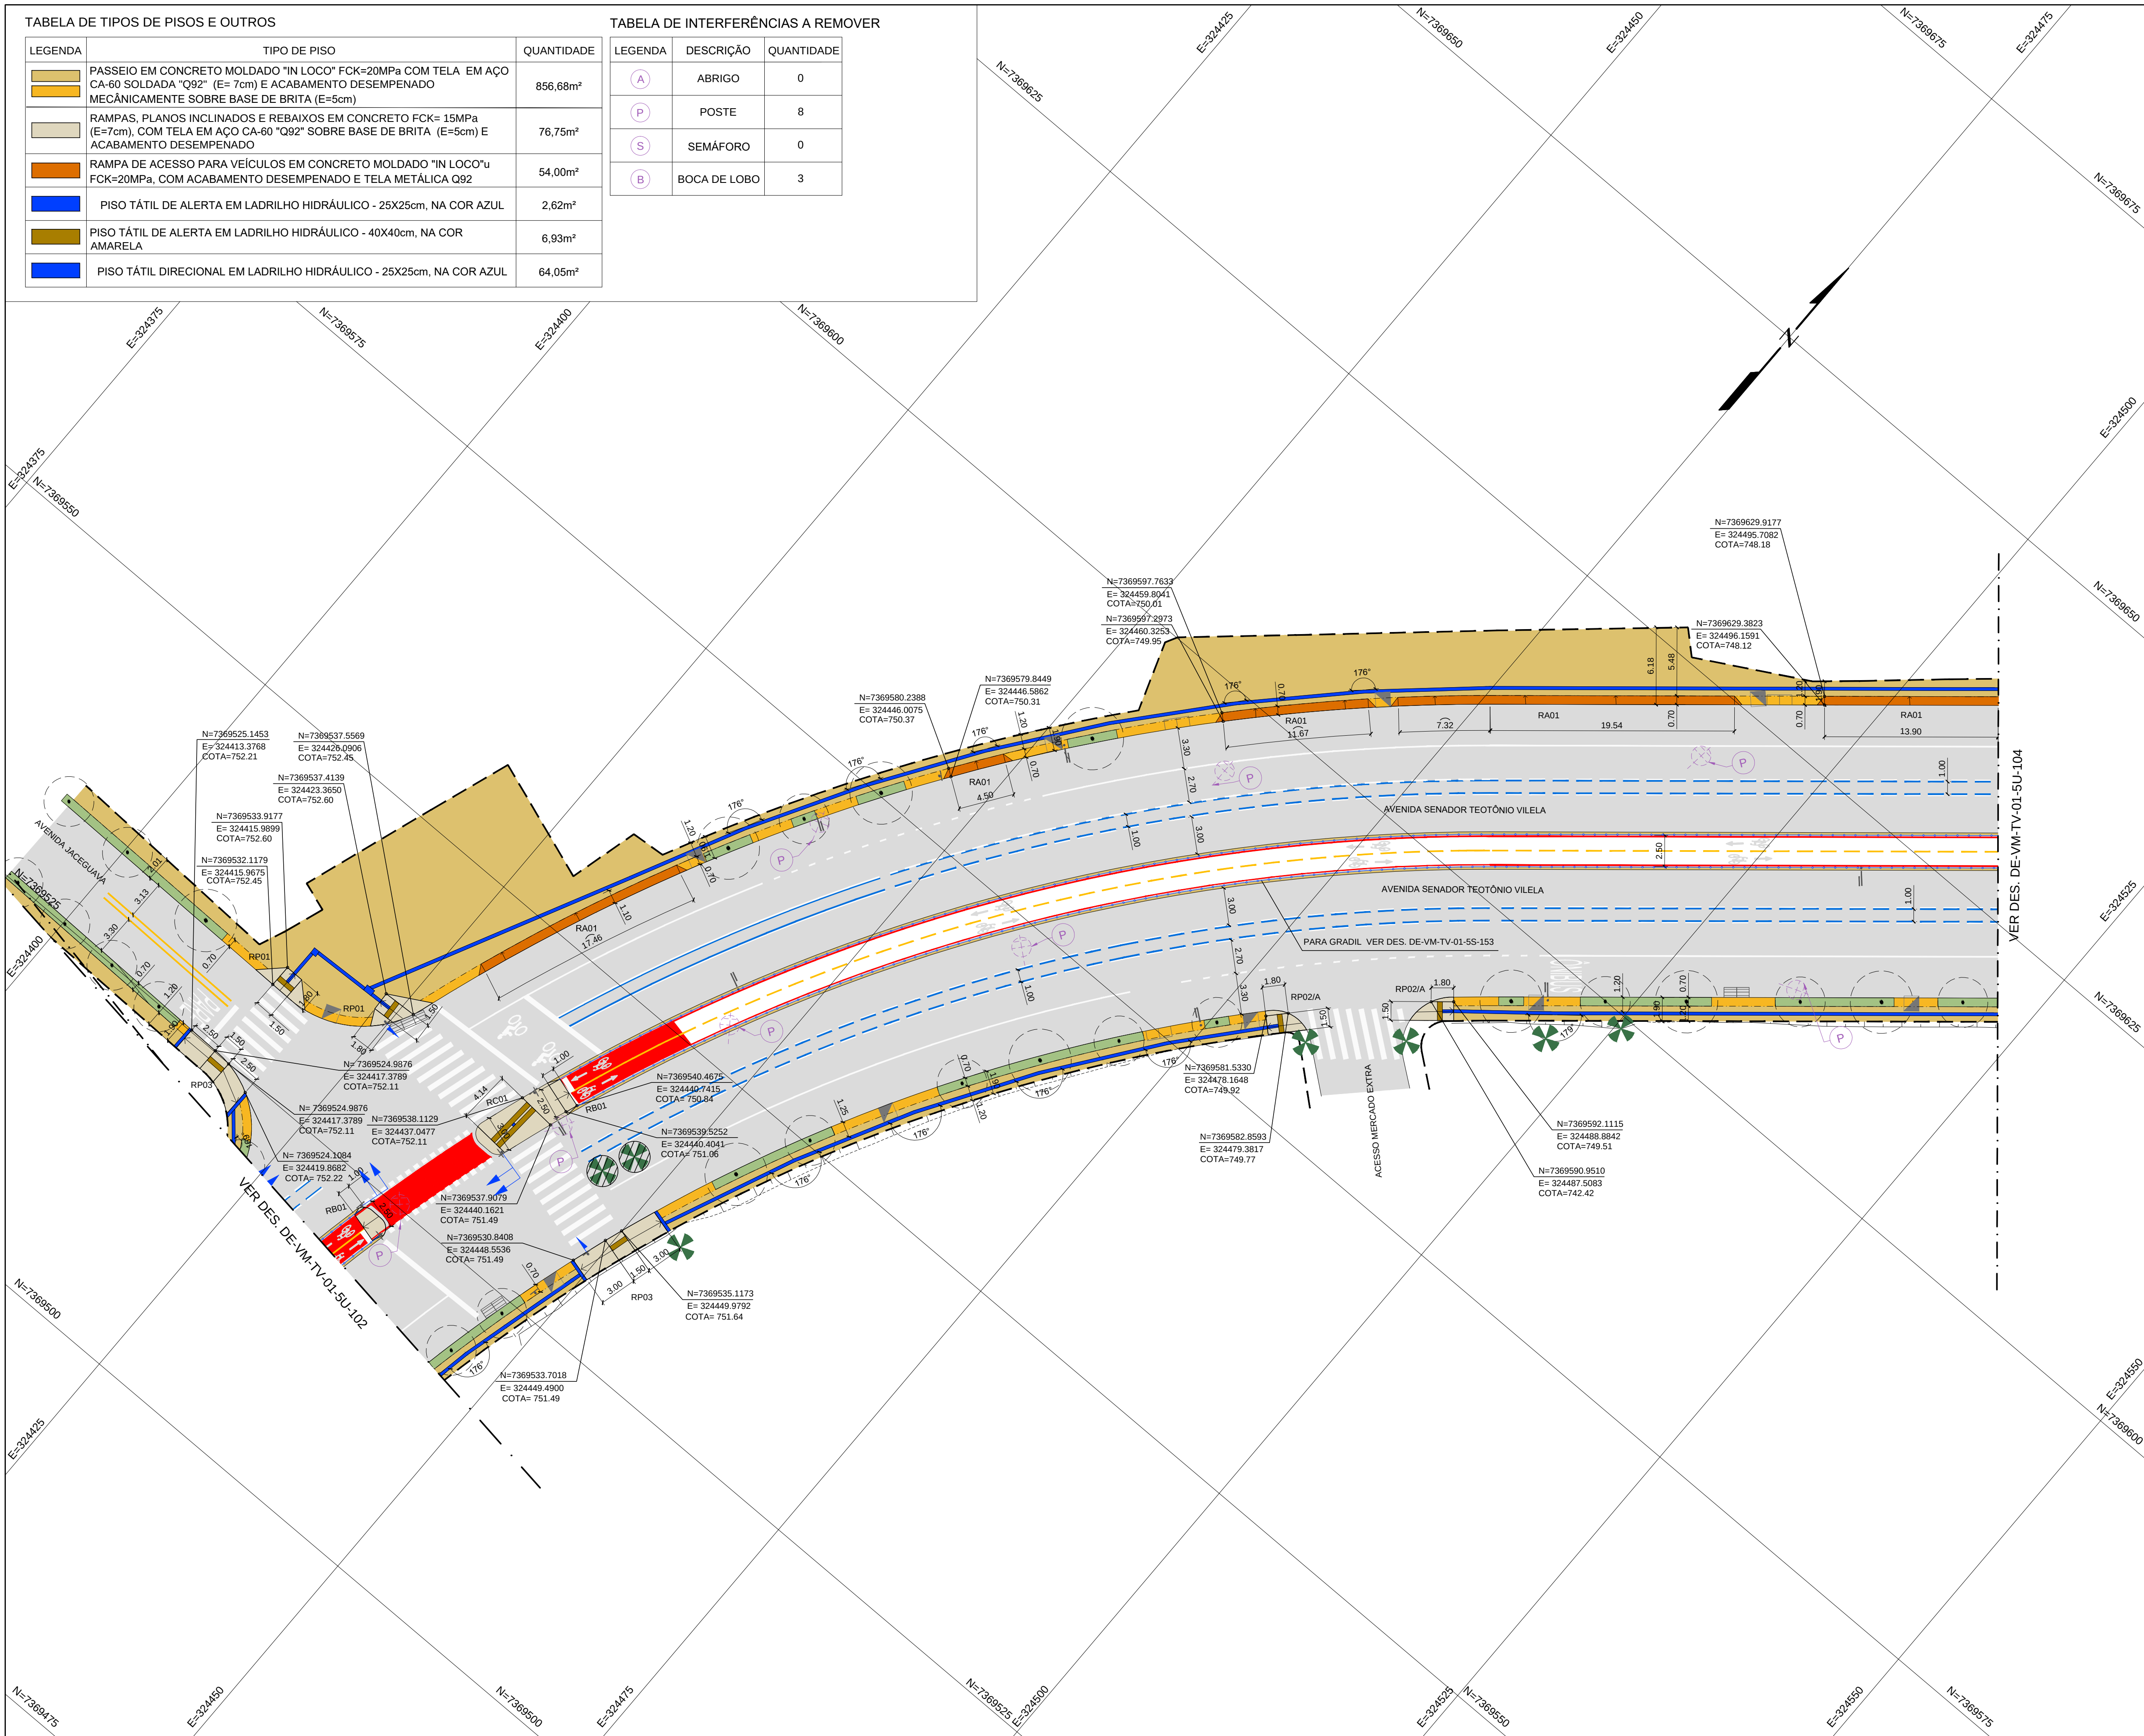


NOTAS:

- 1- MEDIDAS EM METRO, EXCETO ONDE INDICADO.
- 2- PARA AS ROTAS DE PISO PODOTÁTIL FORAM CONSIDERADAS AS NBR 16.537/2018 QUE DISPÕE SOBRE ACESSIBILIDADE - SINALIZAÇÃO TÁTIL DE PISO - DIRETRIZES PARA ELABORAÇÃO DE PROJETOS E INSTALAÇÃO.
- 3- PARA DETALHES DE RAMPA VER FOLHAS DE-VM-TV-014U-007-008;

LEGENDA:

- PISTA
- CORREDOR DE ÔNIBUS
- CICLOVIA
- FAIXA LIVRE
- FAIXA DE ACESSO
- ALINHAMENTO DOS LOTES
- FAIXA AZUL SINALIZAÇÃO
- SEMÁFORO
- PLACAS
- ILUMINAÇÃO
- ÁRVORE PROPOSTA
- CANTEIRO PROPOSTO
- ÁRVORE EXISTENTE A MANTER
- ÁRVORE EXISTENTE A REMOVER
- GRADIL PROPOSTO

ARTICULAÇÃO:

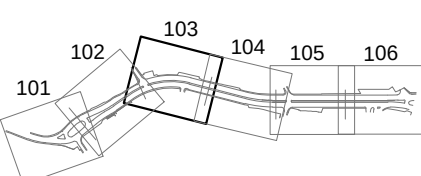

REVISÃO	VISTO PROJETISTA	DATA	VISTO SP OBRAS	DATA
H	FABIOLA	23/06/2026		
G	FABIOLA	02/02/2026		
F	FABIOLA	13/06/2025		
E	FABIOLA	20/09/2024		
D	FABIOLA	16/07/2024		
C	FABIOLA	20/06/2024		
B	FABIOLA	03/04/2024		
A	FABIOLA	04/03/2024		

DESENHOS DE REFERÊNCIA

DE-VM-TV-4F-101 A 103

DE-VM-TV-4F-151 A 153

DOCUMENTOS EXTERNOS DE REFERÊNCIA

DESENHO Nº

V M T V 0 1 5 U 1 0 3 H

SUBSTITUÍDO POR Nº

SUBSTITUI Nº

OBRA

DUPLICAÇÃO VIÁRIA DA AV. SEN. TEOTONIO VILELA.

TÍTULO

PROJETO EXECUTIVO DE URBANISMO - PLANTA

ESCALA



1000-SI060-015-UB3-103_G		
RESPONSÁVEL TÉCNICO		CREA
LEONARDO P. LORENZO		0601838572
VISTO		DATA
PROJETO	FABIOLA AVAMILENO	MAR/2024
DESENHO	FABIOLA AVAMILENO	MAR/2024
VERIFICAÇÃO	ENNIO PASSAFINI	MAR/2024
APROVAÇÃO	JULIANA GODOI	MAR/2024
LIBERAÇÃO	LEONARDO P. LORENZO	MAR/2024

SP Obras
CONSTRUINDO A SÃO PAULO DO FUTURO

ESTE DESENHO É PROPRIEDADE DA SP OBRAS. NÃO PODENDO SER REPRODUZIDO E/OU REVELADO NO TODO OU EM PARTE SEM SUA AUTORIZAÇÃO.

APROVAÇÃO FINAL	DATA
VERIFICAÇÃO	
APROVAÇÃO	
LIBERAÇÃO	